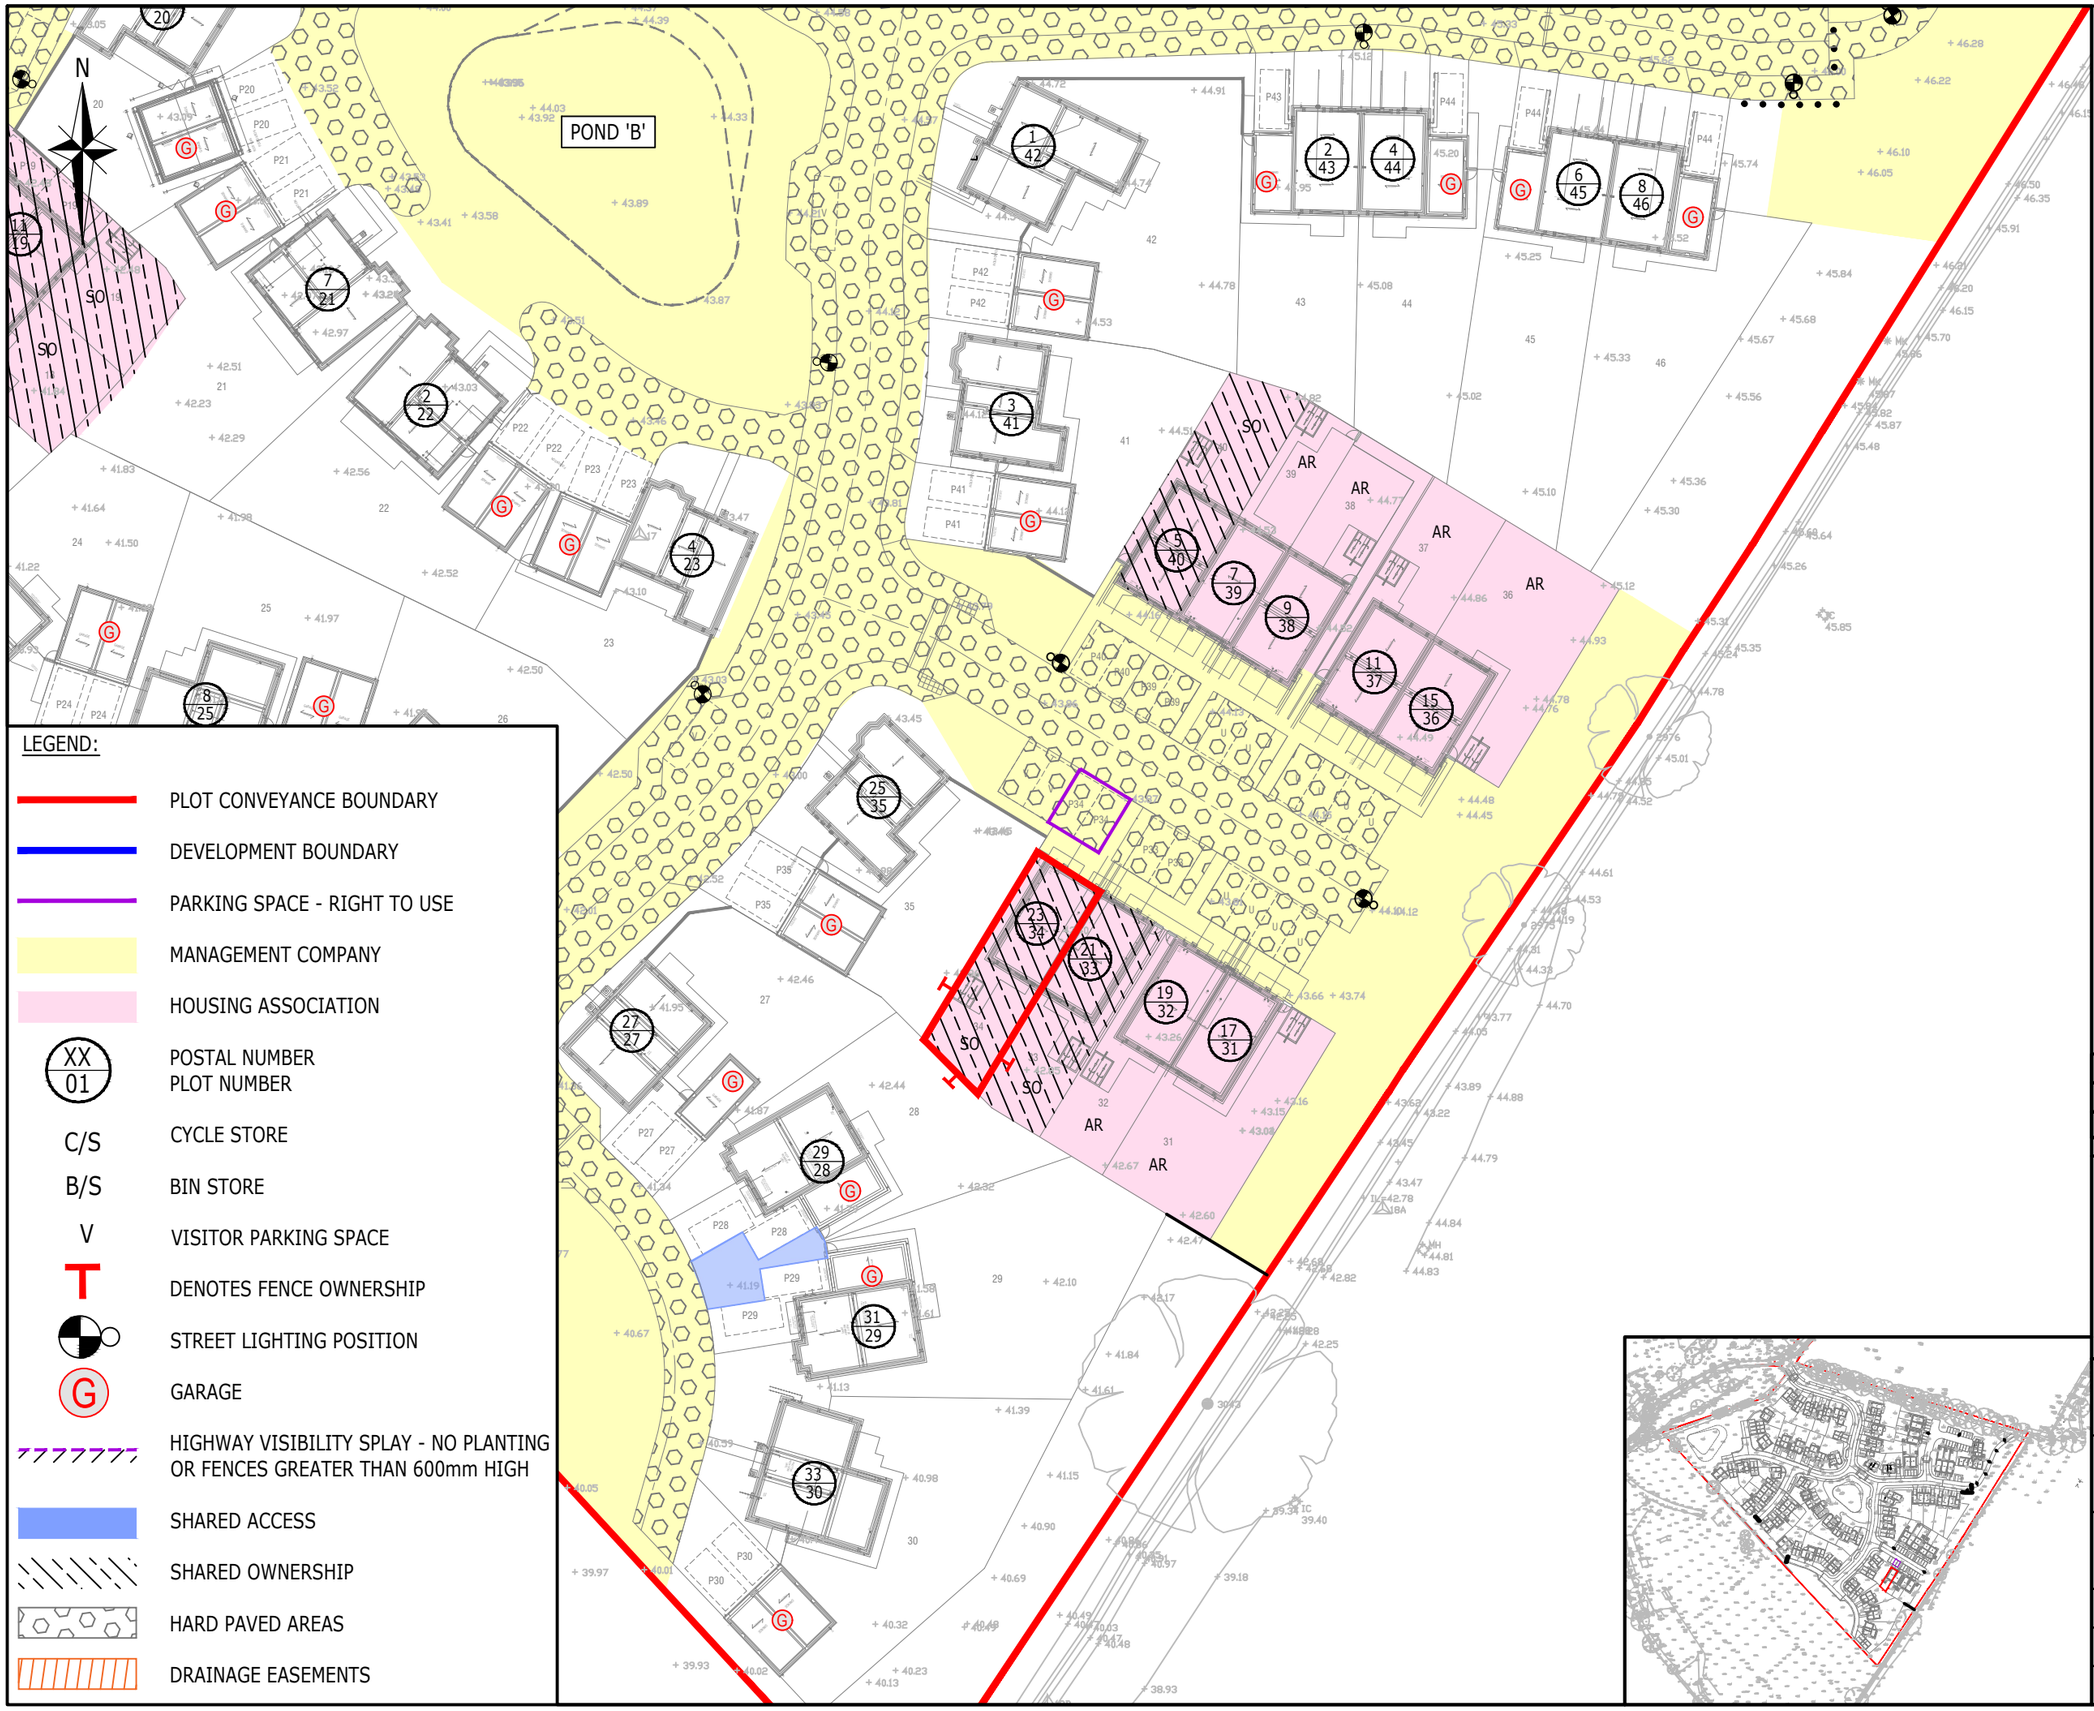

LEGEND:

- PLOT CONVEYANCE BOUNDARY
- DEVELOPMENT BOUNDARY
- PARKING SPACE - RIGHT TO USE
- MANAGEMENT COMPANY
- HOUSING ASSOCIATION
- XX / 01 — POSTAL NUMBER / PLOT NUMBER
- C/S — CYCLE STORE
- B/S — BIN STORE
- V — VISITOR PARKING SPACE
- T — DENOTES FENCE OWNERSHIP
- STREET LIGHTING POSITION
- G — GARAGE
- HIGHWAY VISIBILITY SPLAY - NO PLANTING OR FENCES GREATER THAN 600mm HIGH
- SHARED ACCESS
- SHARED OWNERSHIP
- HARD PAVED AREAS
- DRAINAGE EASEMENTS

GENERAL NOTES:

1. THIS DRAWING IS TO BE READ IN CONJUNCTION WITH ALL OTHER RELATED DRAWINGS ISSUED BY THE ENGINEER.

2. ALL DIMENSIONS SHOWN ON THIS DRAWING ARE IN METRES, UNLESS OTHERWISE STATED.

3. ALL DIMENSIONS, LEVELS AND SURVEY GRID CO-ORDINATES ARE TO BE CHECKED ON SITE AND THE ENGINEER NOTIFIED IMMEDIATELY OF ANY DISCREPANCIES PRIOR TO THE COMMENCEMENT OF THE WORKS.

4. NO DEVIATION FROM THE DETAILS SHOWN ON THIS DRAWING IS PERMITTED WITHOUT PRIOR PERMISSION FROM THE ENGINEER.

0m — 25m

Scale: 1:500 @A3

FOR INFORMATION ONLY

PLAN 1

Rev	Description	Drn	Chk	App	Date
P4	BOUNDARY AROUND UNALLOCATED SPACES REMOVED FOLLOWING CLIENT COMMENTS	MJR	MJR	JEC	10.11.20
P3	SHARED OWNERSHIP & HARD PAVED HATCH ADDED. POSTAL NUMBERS AND STREET NAMES ADDED.	AMG	JM	GJH	12.06.20
P2	UPDATED TO SUIT OVERALL CONVEYANCE PLAN	JS	JM	GJH	24.03.20

ARDENT CONSULTING ENGINEERS

Third Floor
The Hallmark Building
52-56 Leadenhall Street
London
EC3M 5JE

Tel: 020 7680 4088
Web: www.ardent-ce.co.uk
E-mail: enquiries@ardent-ce.co.uk

Client

Crest Nicholson South
Crest House
Pyrcroft Road
Chertsey
Surrey
KT16 9GN

Project Title:

BISHOPS WALTHAM (PHASE 2)

Drawing Title:

CONVEYANCE PLAN - PLOT 34

A3 Scale	Date	Designed by
1:500	OCT 2019	JM
Drawn by	**Checked by**	**Approved by**
UN	JM	GH

Drawing Number: 14773-6034 — Rev: P4

user name: millie rickleton

File Location: y:\ardent projects\181670 - bishops waltham phase 2 (detailed design)\technical\acad\drawings\181670_6000 overall conveyance plan.dwg