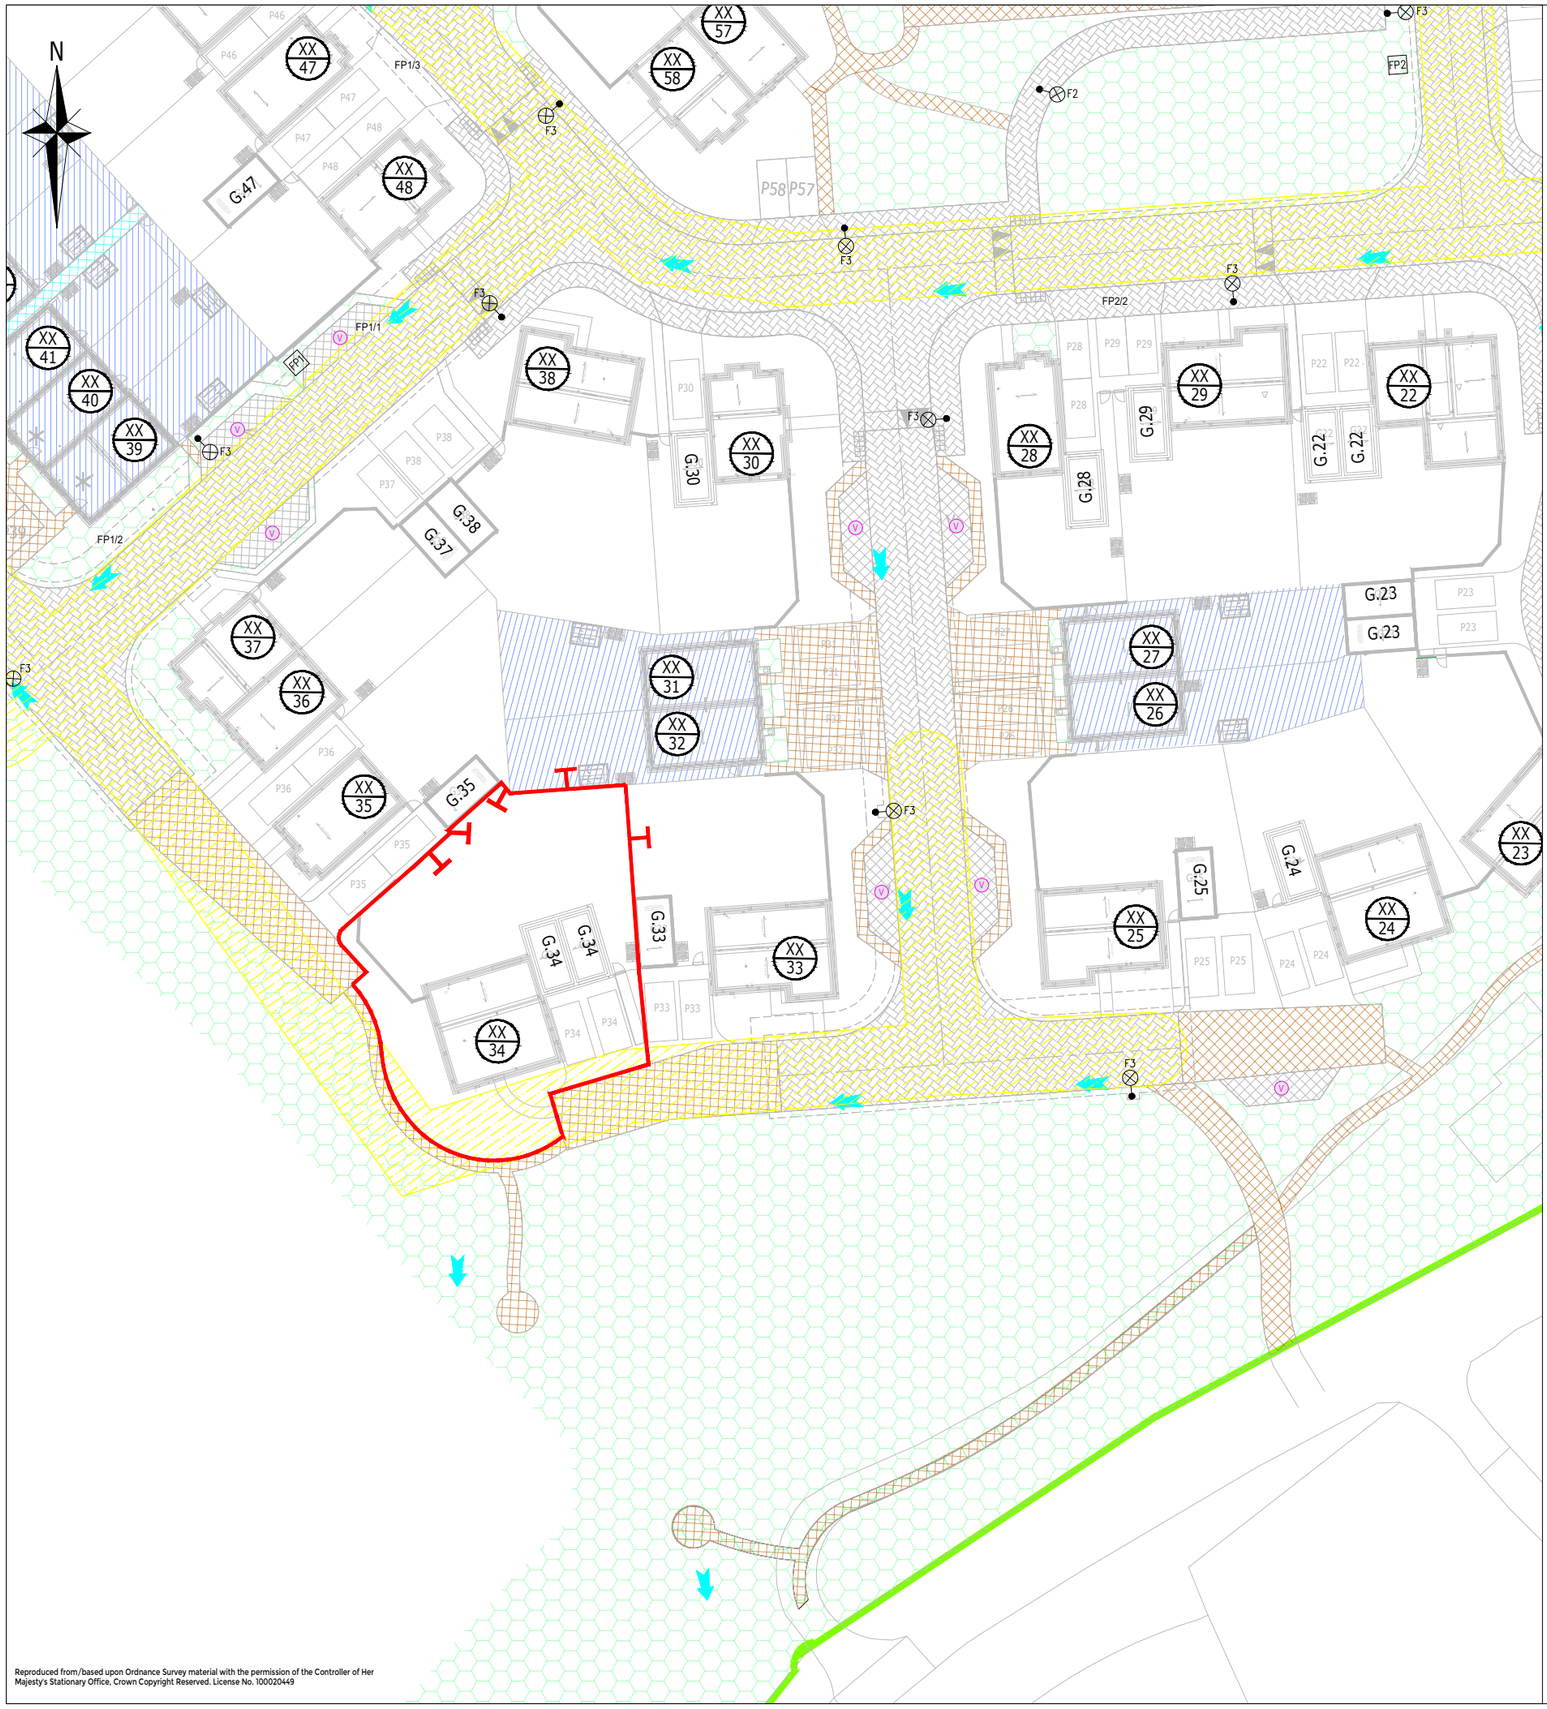

Reproduced from/based upon Ordnance Survey material with the permission of the Controller of Her Majesty's Stationary Office, Crown Copyright Reserved. License No. 100020449

LEGEND:

- OPEN SPACES TO BE MAINTAINED BY MANAGEMENT COMPANY
- HOUSING ASSOCIATION
- RIGHTS TO PARK TO BE MAINTAINED BY MANAGEMENT COMPANY.
- FOUL WATER PUMPING STATION TO BE TRANSFERRED TO SOUTHERN WATER
- EXISTING THAMES WATER EASEMENT
- PROPOSED THAMES WATER S104 EASEMENT
- SHARED ACCESS
- PRIVATE ESTATE ROADS (MANAGEMENT COMPANY)
- MAINTAINED HARDSTANDING/VERGE BY MANAGEMENT CO.
- MAINTAINED VISITOR PARKING SPACES BY MANAGEMENT CO.
- HIGHWAYS ADOPTABLE CARRIAGEWAY (S278)
- T — DENOTES FENCE OWNERSHIP
- PLOT BOUNDARY
- SITE BOUNDARY
- P.54 — PARKING FOR PLOT NUMBERED
- G.61 — GARAGE FOR PLOT NUMBERED
- V — VISITOR PARKING
- XX 14 — POSTAL NUMBER PLOT NUMBER
- F2 — STREET LIGHTING

GENERAL NOTES:

1. THIS DRAWING IS TO BE READ IN CONJUNCTION WITH ALL OTHER RELATED DRAWINGS ISSUED BY THE ENGINEER.
2. ALL DIMENSIONS SHOWN ON THIS DRAWING ARE IN METRES, UNLESS OTHERWISE STATED.
3. ALL DIMENSIONS, LEVELS AND SURVEY GRID CODPORDINATES ARE TO BE CHECKED ON SITE AND THE ENGINEER NOTIFIED IMMEDIATELY OF ANY DISCREPANCIES PRIOR TO THE COMMENCEMENT OF THE WORKS.
4. NO DEVIATION FROM THE DETAILS SHOWN ON THIS DRAWING IS PERMITTED WITHOUT PRIOR PERMISSION FROM THE ENGINEER.

0m 5m 25m

Scale: 1:500 @ A3

Rev	Description	Drn	Chk	App	Date
P3	PLOT 34,35 CORRECTED AT CORNER OF GARAGE	ME	BW	BW	13.12.2023
P2	PLOTS 17,18, 39,40,55,56,58 BOUNDARY UPDATES	ME	DAM	DP	22.06.2022
P1	ISSUED FOR INFORMATION	ME	DAM	DP	27.05.2022

ARDENT CONSULTING ENGINEERS

Suite 207
One Alie Street
London
E1 8DE

Tel: 020 7680 4088
Fax: 020 7488 3736

Web: www.ardent-ce.co.uk
E-mail: enquiries@ardent-ce.co.uk

Client

Crest Nicholson South
Crest House
Pyrcroft Road
Chertsey
Surrey
KT16 9GN

Project Title:

BISHOPS WALTHAM

Drawing Title:

CONVEYANCE PLAN
PLOT 34

A3 Scale	Date	Designed by
1:500	MAY 2022	ME
Drawn by	**Checked by**	**Approved by**
ME	DAM	DP

Drawing Number 2002441-6034 Rev P3