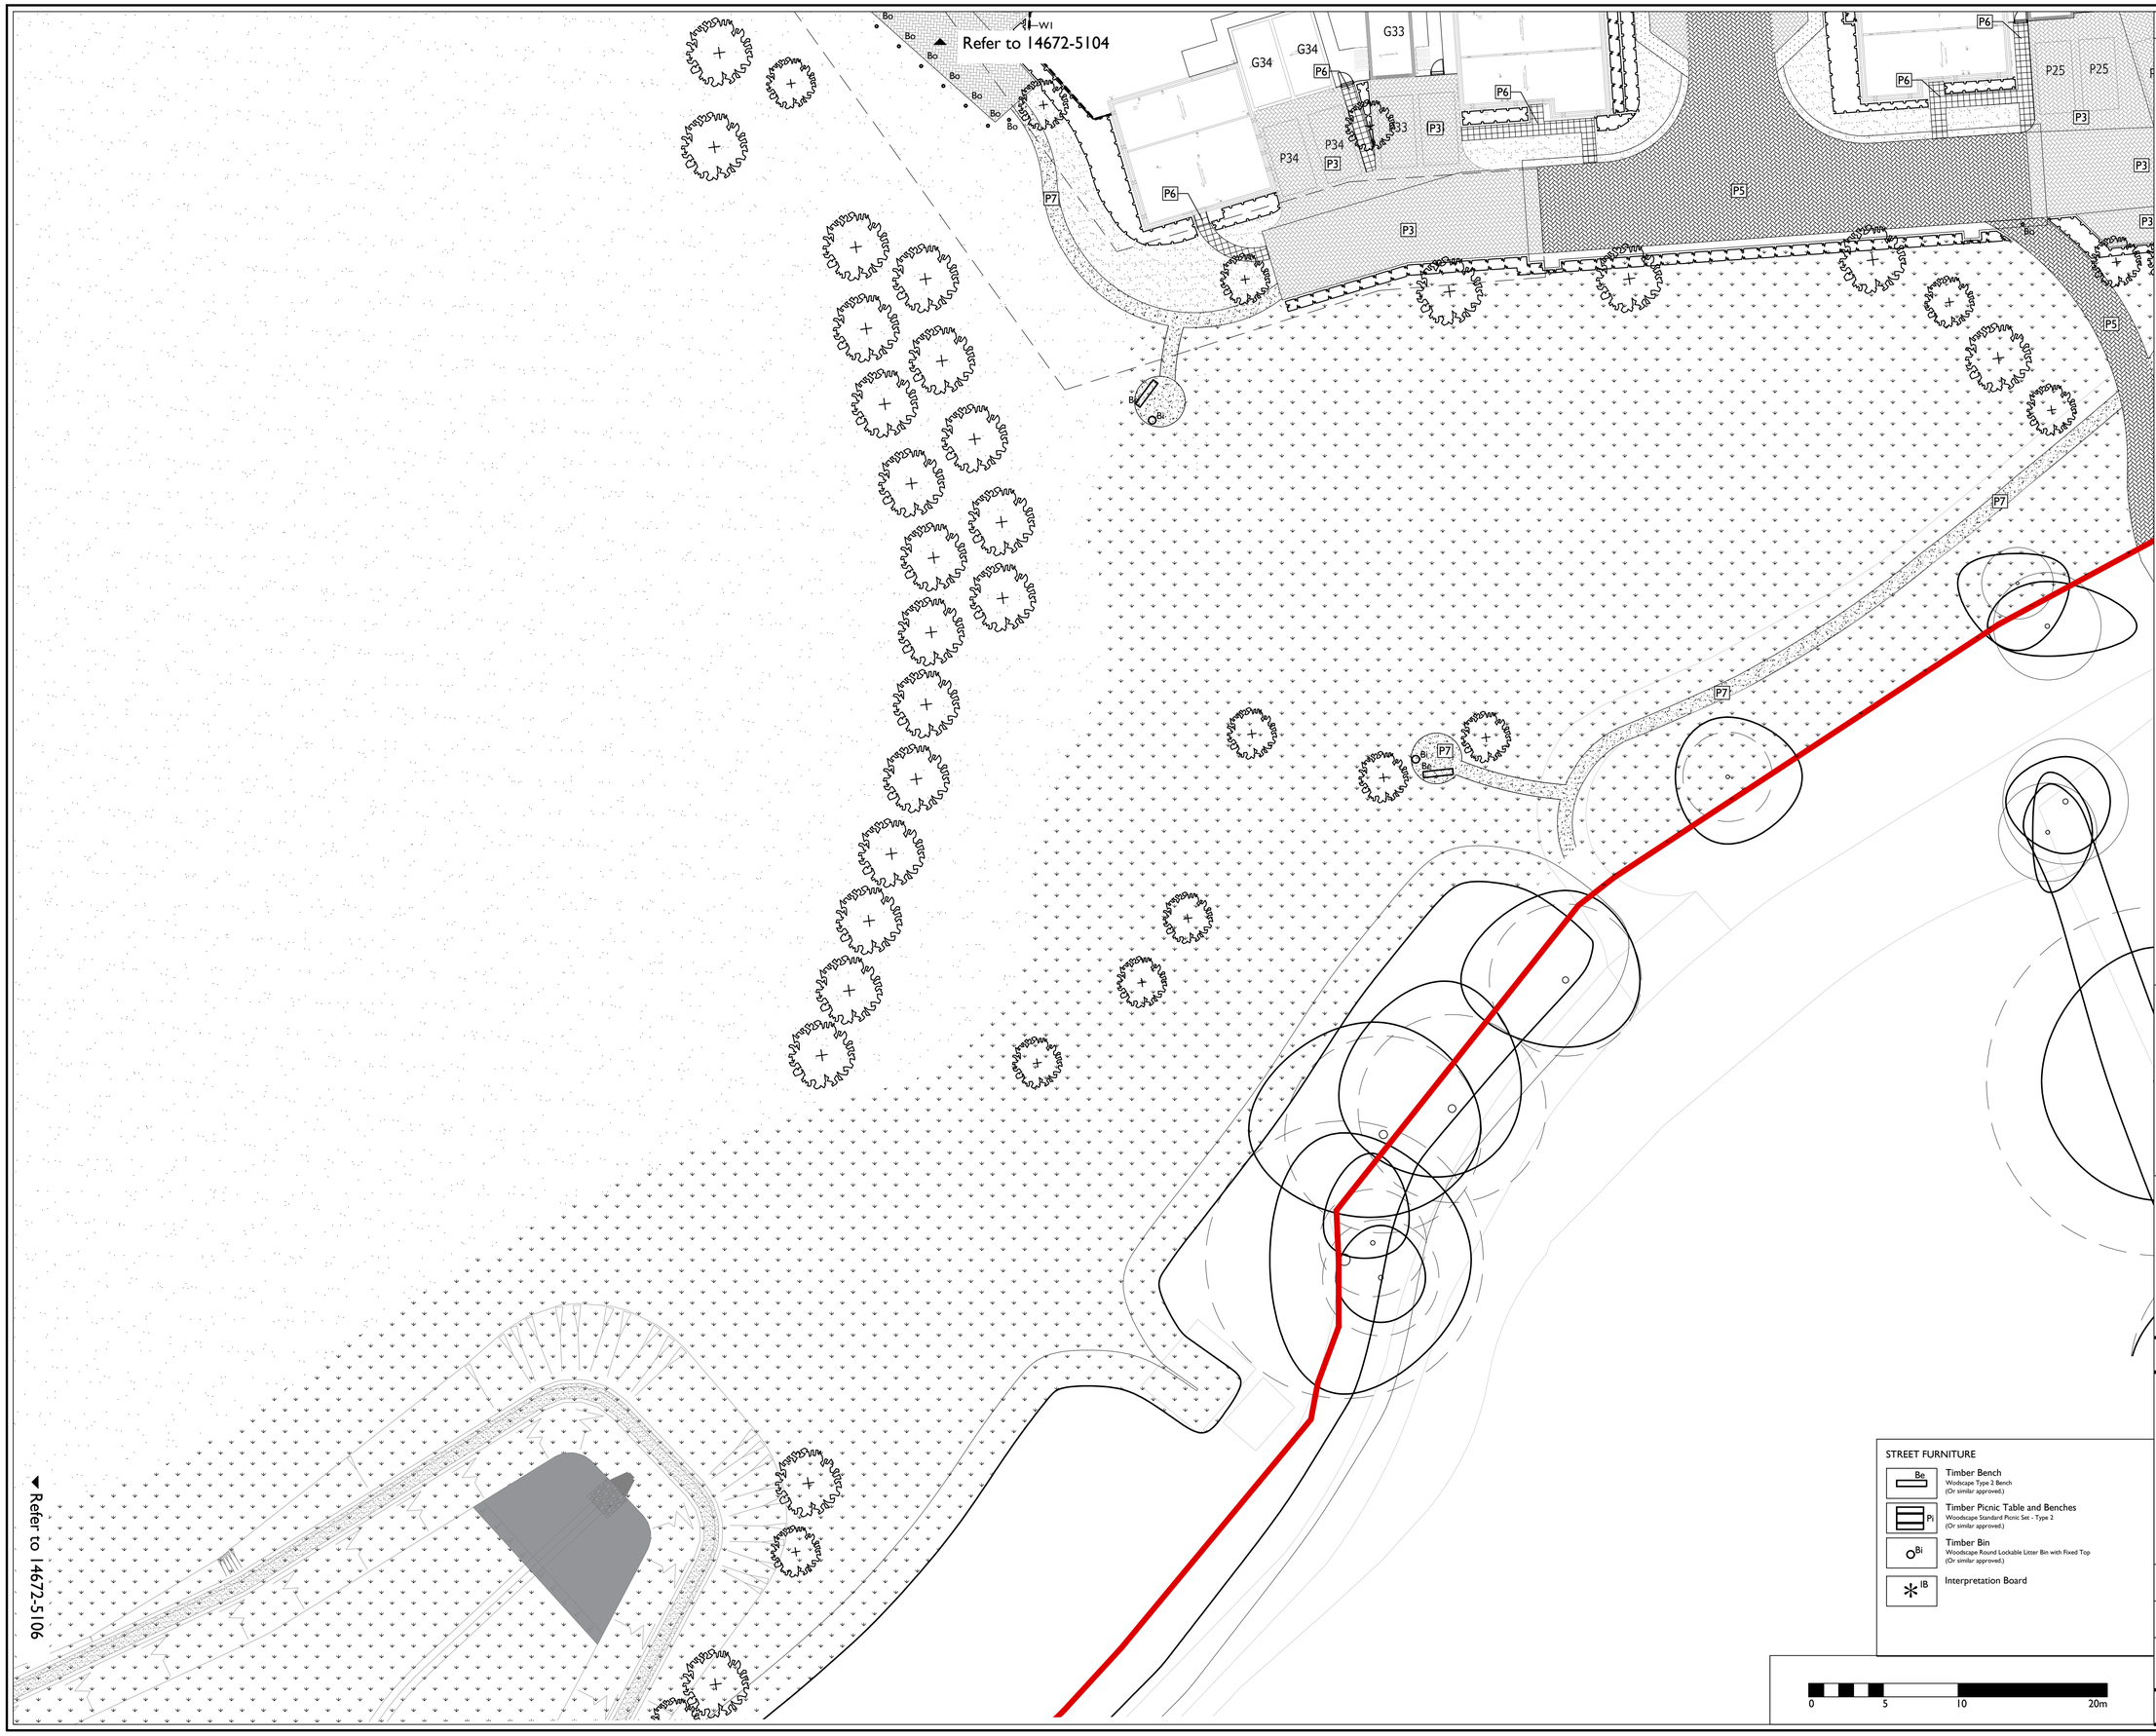

APAL FILE REFERENCE
2583-LA-01-08.dwg

Notes
This drawing is subject to copyright.
Do not scale from this drawing.

Based on drawing by ARDENT
Drawing number 14672-940-P1

North

LEGEND

Application Boundary

SOFT LANDSCAPE

- Existing Trees
- Proposed hedgerow
- Proposed trees (18-20cm girth)
- Proposed Grass Refer to Planting Plans
- Proposed fruit trees (18-20cm girth)
- Proposed Wildflower Meadow
- Proposed ornamental planting

HARD LANDSCAPE

- P1 Bituminous Standard Black Surface Course Finish
- P2 Bituminous Footway Standard Black Surface Course Finish
- P3 Marshalls Key Blok Vintage 'Brindle' Block paving, 200x100x80mm to private driveways or similar approved
- P4 Marshalls Tegula Block Paving 'Harvest' 160 gauge x 80mm to Mews Courts or similar approved
- P5 Marshalls Key Blok Vintage 'Burnt Ochre' Block paving, 200x100x80mm to Cycle Route or similar approved
- P6 Marshalls Renaissance 'Chalkstone' lightly textured flag paving: 400x400mm to private paths
- P7 Breedon self binding gravel 'Golden Amber' to public open spaces or similar approved

BOUNDARY TREATMENTS

- W1 - 1800mm Brick Wall
  Ibstock Surrey Orange (Code 4131)
  (Refer to Architect's details)
- W2 - 1800mm Brick Wall
  Ibstock Surrey Red Multi (Code 4133)
  (Refer to Architect's details)
- W3 - 1800mm Brick Wall
  Ibstock Surrey County Red (Code 4132)
  (Refer to Architect's details)
- 1800mm Close Board Fence
- ER 1215mm Estate Railings
  Black powder coated
- Bo Timber Bollards
  Woodscape Round Hardwood Timber Bollards: Flat top, height 1000mm above ground (1500mm in total), width 175mm, no groove (Or similar approved.)

STREET FURNITURE

- Be Timber Bench
  Wodscape Type 2 Bench
  (Or similar approved.)
- Pi Timber Picnic Table and Benches
  Woodscape Standard Picnic Set - Type 2
  (Or similar approved.)
- Bi Timber Bin
  Woodscape Round Lockable Litter Bin with Fixed Top
  (Or similar approved.)
- IB Interpretation Board

0 5 10 20m

KEY PLAN

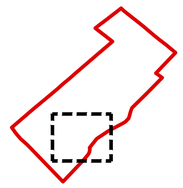

Rev	Description	Date	Drawn	Checked
T2	Update to basin	06/04/23	JH	JH
T1	Updated to Tender following layout changes	07/07/21	BI	JH
P2	Legend updated	07/12/17	JH	JH
P1	Updated to latest layout	24/11/17	AC	JH
P0	Draft for comment		AC	JH

Drawing Status
TENDER

Allen Pyke Associates
Landscape architecture Urban design Environmental planning
The Factory, 2 Acre Road,
Kingston upon Thames,
Surrey KT2 6EF
T 020 8549 3434 F 020 8547 1075
www.allenpyke.co.uk
KINGSTON UPON THAMES • CAMBRIDGE
A registered practice of the Landscape Institute

Client
Crest Nicholson

Scale
1:200@A1

Project
Tangier Lane, Bishop Waltham

By/Chk
AC/JH

Drawing Title
Landscape General Arrangements
6 of 8

Date
14/08/17

Drawing Number
14672-5105

Revision
T2