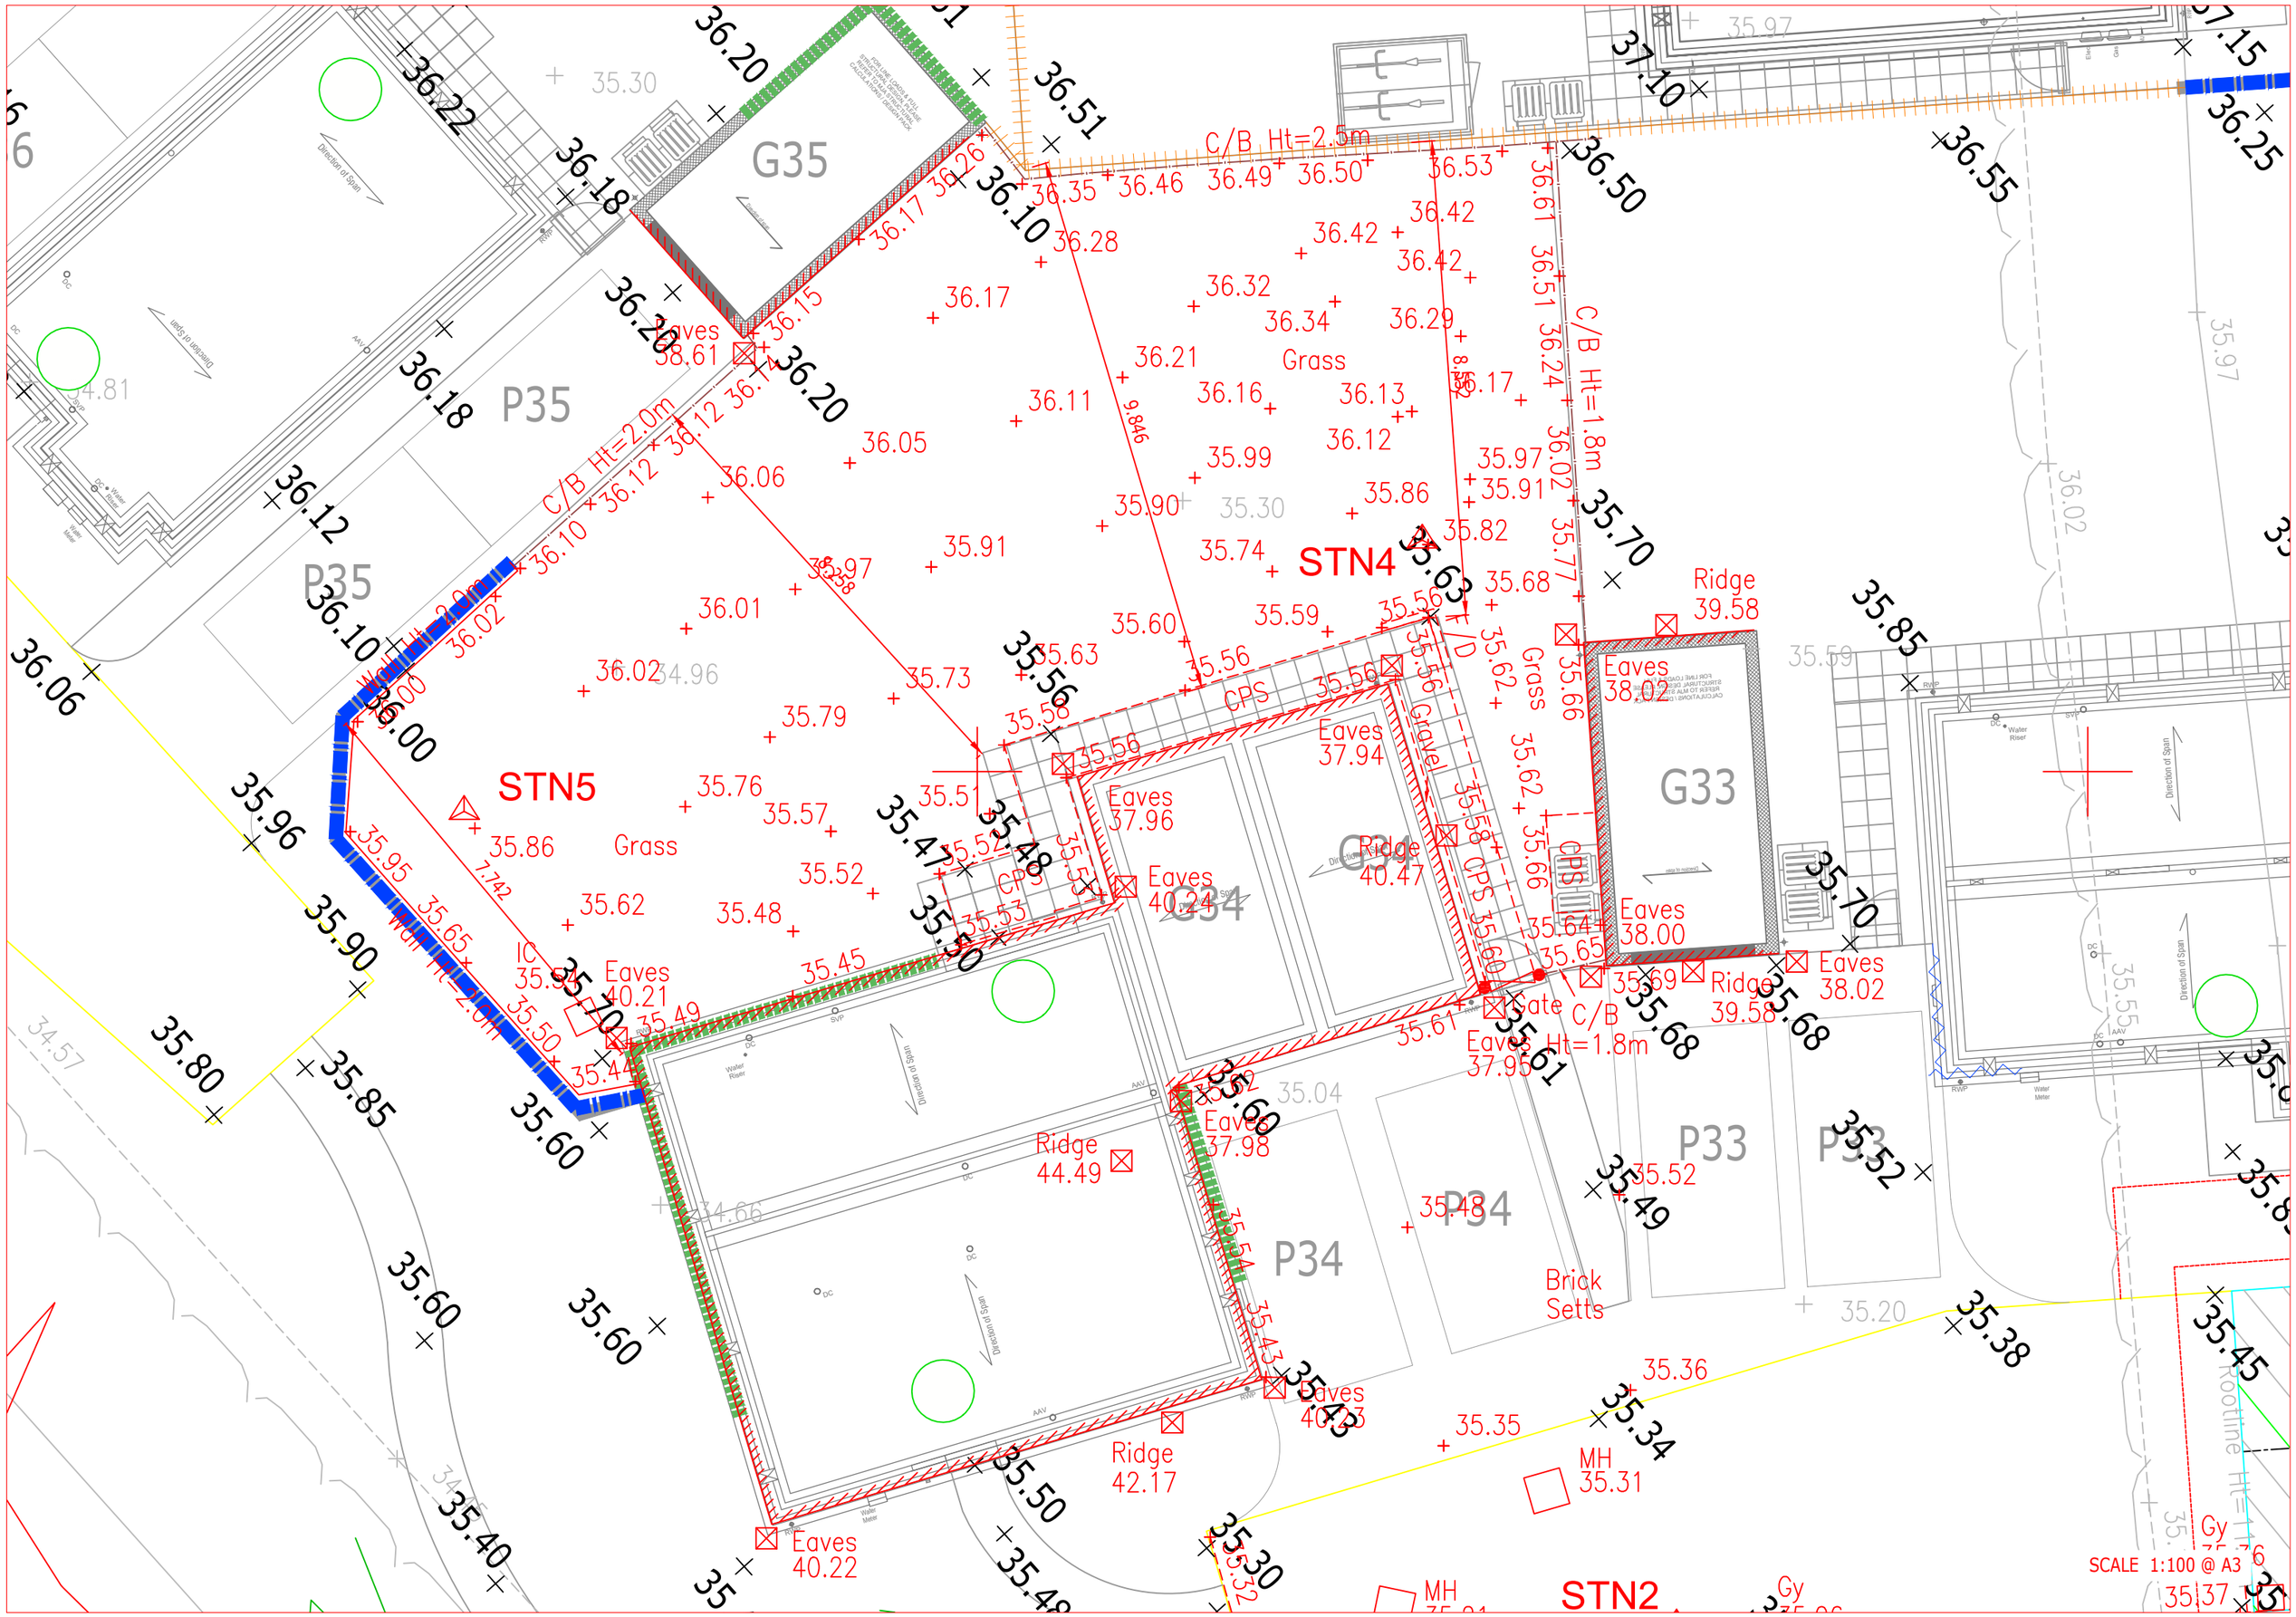
G35
P35
P35
STN4
STN5
STN2
C/B Ht=2.5m
C/B Ht=2.0m
C/B Ht=1.8m
Wall Ht=2.0m
Eaves
38.61
Grass
Ridge
39.58
Eaves
38.05
Eaves
37.94
Eaves
37.96
Eaves
40.24
Ridge
40.47
Eaves
38.00
Eaves
38.02
Ridge
39.58
Eaves
40.21
Ridge
44.49
Eaves
37.98
Ridge
42.17
Eaves
40.22
Eaves
37.95
Gate
Brick
Setts
MH
35.31
CPS
Gravel
G33
G34
P33
P34
Rootline Ht=1.76
SCALE 1:100 @ A3