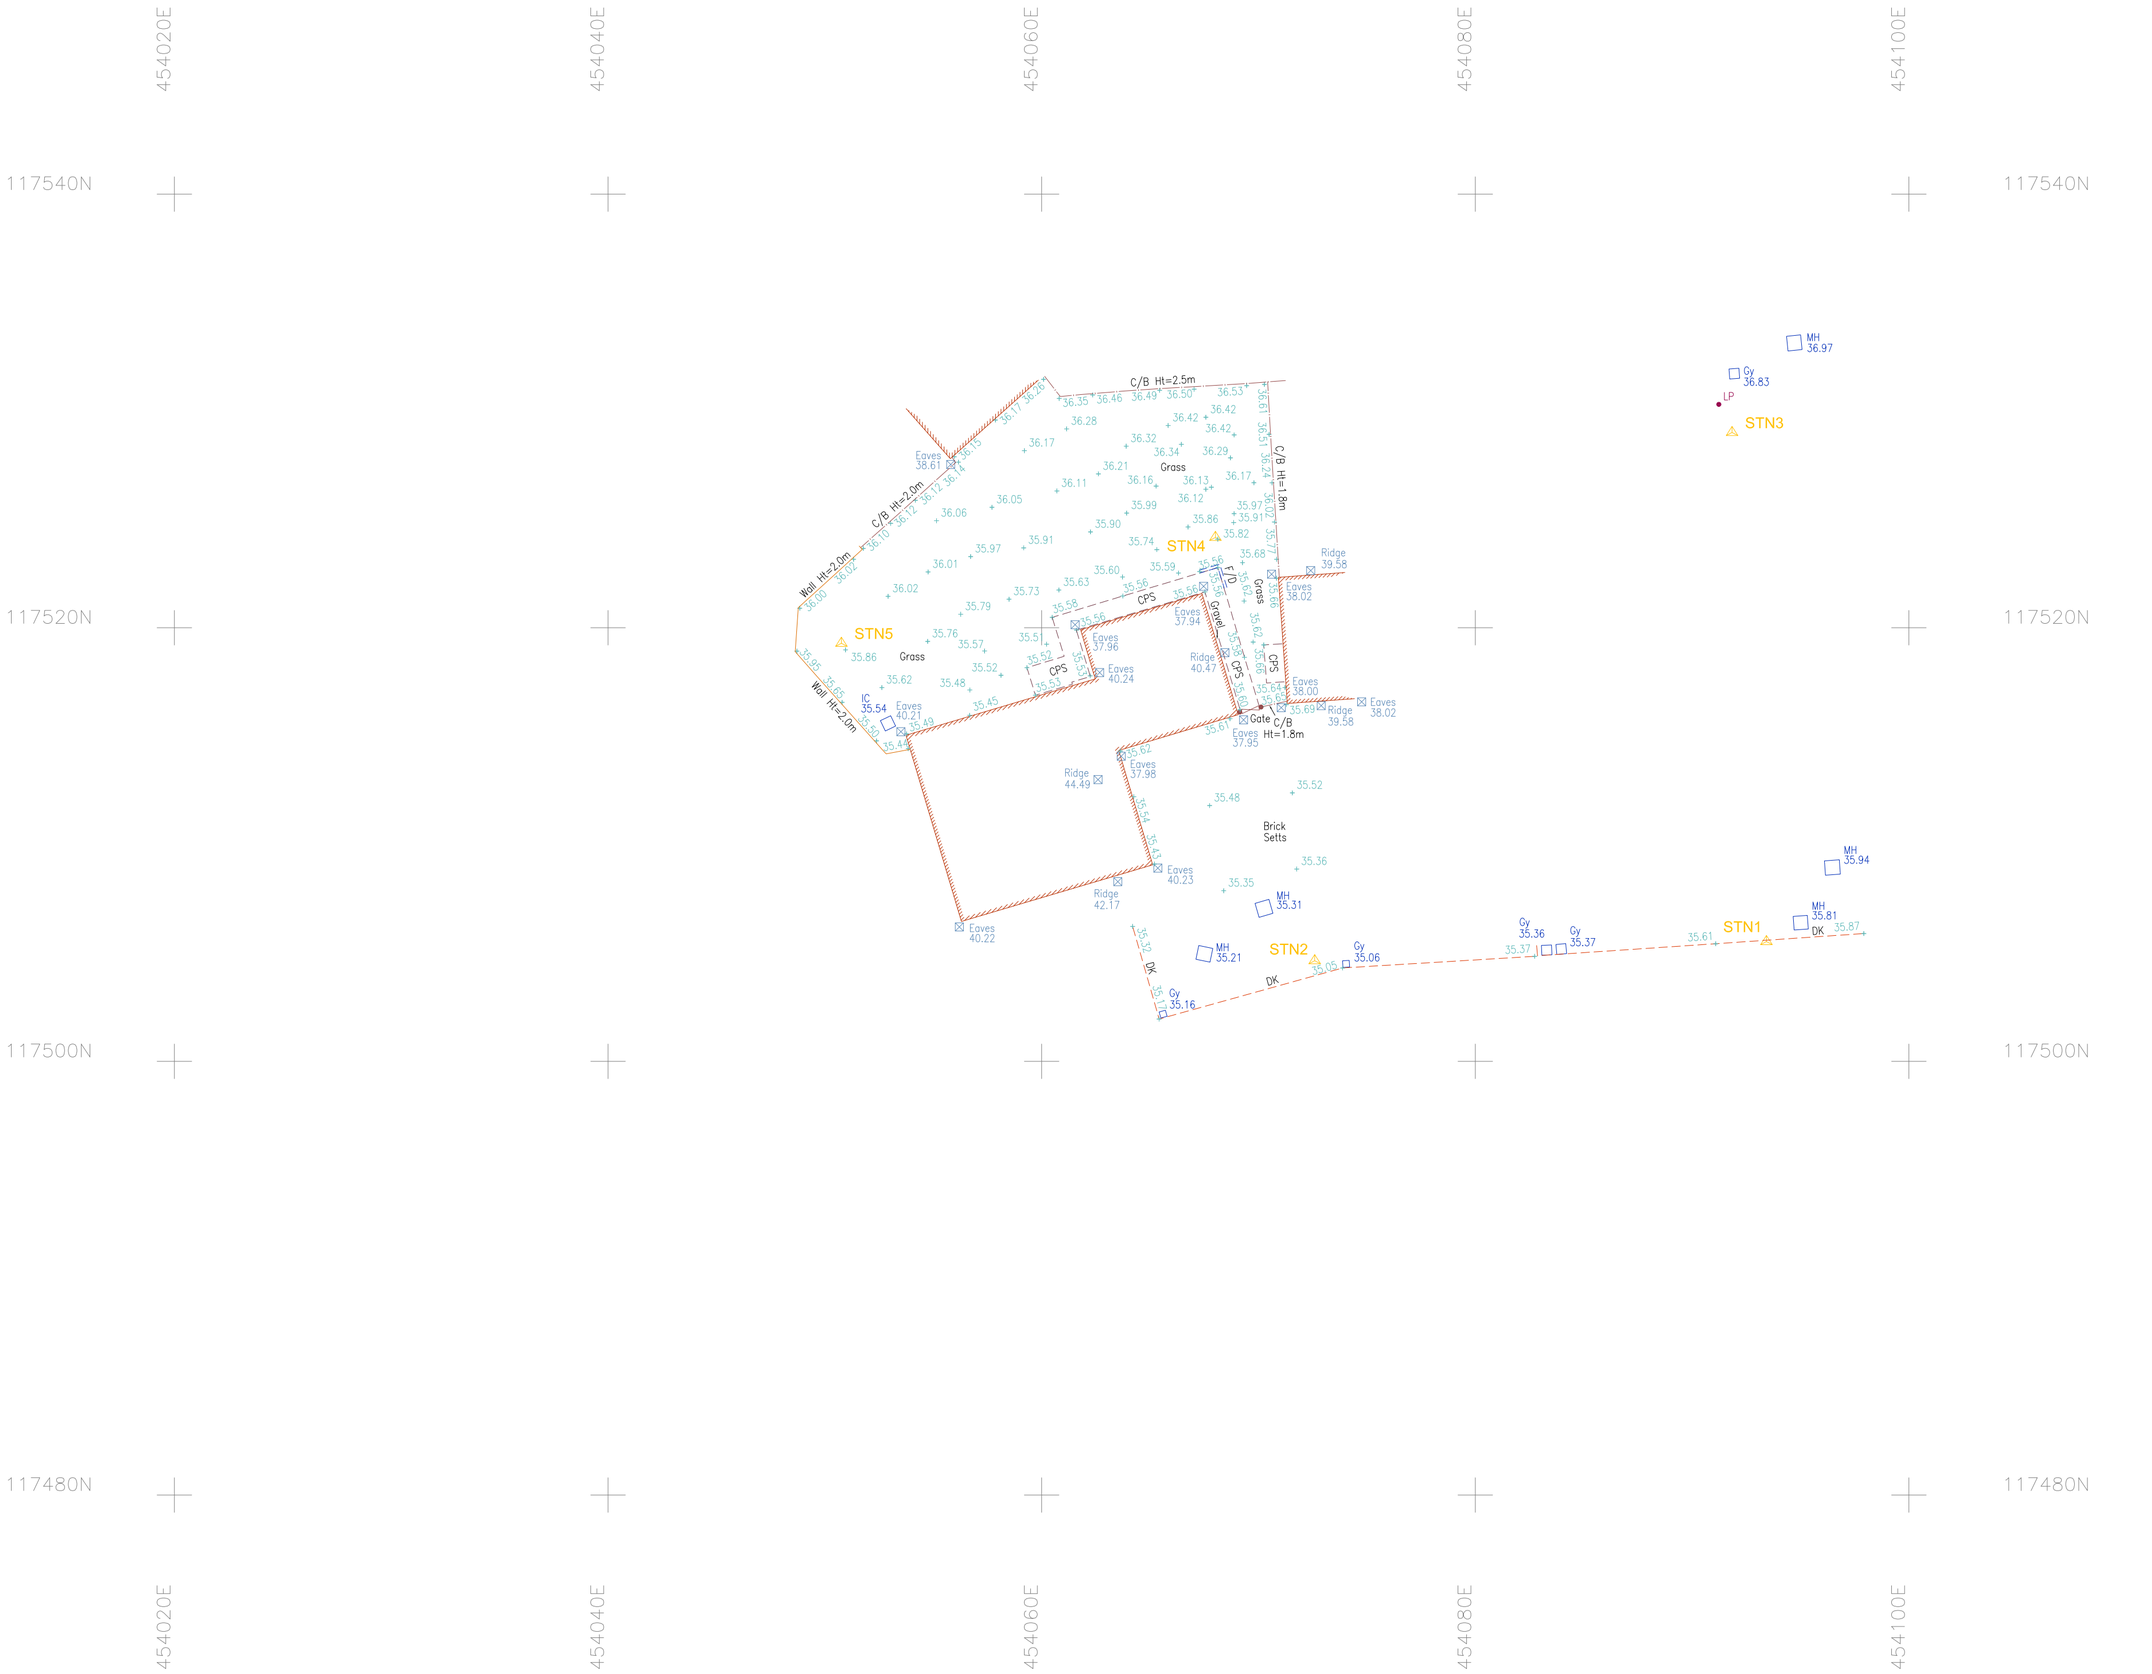

Notes:

All information contained in this drawing (including digital data) should be checked and verified prior to any fabrication or construction.

Grid coordinates are based on an OS GNSS system on a plane grid with a scale factor of 1.0000.

INDICATIVE

Legend:

Fences
Walls
Hedges
Trees
Buildings
Overhead Electric
Overhead Phone
Gate

Fences:

Barbed Wire Fence	B/W
Corrugated Iron Fence	C/I
Closed Board Fence	C/B
Chestnut Paling Fence	C/P
Iron Railing Fence	I/R
Post and Chain Fence	P/C
Post and Rail Fence	P/R
Post Wire Fence	P/W
Interwoven	I/W
Chain Link Fence	C/L
Larch Lap Fence	L/L
Wire Mesh Fence	W/M

Abbreviations:

BOLLARD	BO	MARKER	MK
BRITISH TELECOM IC	BT	PARKING METER	PM
CONCRETE PAVING SLABS	CPS	ROAD NAME PLATE	RNP
COVER LEVEL	CL	ROAD SIGN	RS
DROP KERB	DK	RODDING EYE	RE
ELECTRICITY POLE	EP	RETAINING WALL	Rtw
FIRE HYDRANT	FH	RAINWATER PIPE	RWP
FLOWER BED	F/B	SOIL VENT PIPE	SVP
FOOTPATH	FP	STOP VALVE	SV
GAS VALVE	GV	TELEGRAPH POLE	TP
CCELT	CY	TRAFFIC LIGHT	TL
INSPECTION COVER	IC	UNABLE TO LIFT	UTL
PIPE INVERT LEVEL	IL	VENT PIPE	VP
KERB OUTLET	KO	WATER METER	WM
MAN HOLE	MH		

Coordinate Table

Stn	Easting	Northing	Level
STN1	454093.429	117505.524	35.718
STN2	454072.593	117504.642	35.096
STN3	454091.844	117529.004	36.746
STN4	454068.014	117524.167	36.014
STN5	454050.764	117519.284	36.078

Rev. Suffix	Date	Initial	Revision Details

Surveyor	LW	Verified By	LW	CAD Operator	EG	Approved By	AL	Date	21.03.24

Levelling GNSS Datum OSGB36

To an OS GNSS Datum

Client

Crest NICHOLSON

Location

Plot 34, Arbany Wood, Bishops Waltham, Southampton

Drawing Title

Topographical Survey

Job No. 2403019	Old Job No.
Drawing Number CN/2403019	Revision Suffix
Scale 1:200m (A2)	Date March 2024

CD SURVEYS LTD
LAND, BUILDING & SITE ENGINEERING
PENTIRE - STABLE 1
FORDBRIDGE ROAD,
SUNBURY-ON-THAMES
MIDDLESEX, TW16 6AX
Tel (01932) 761196
Fax (01932) 786419
Email: mail@cdsurveys.com
Visit us at: www.cdsurveys.com